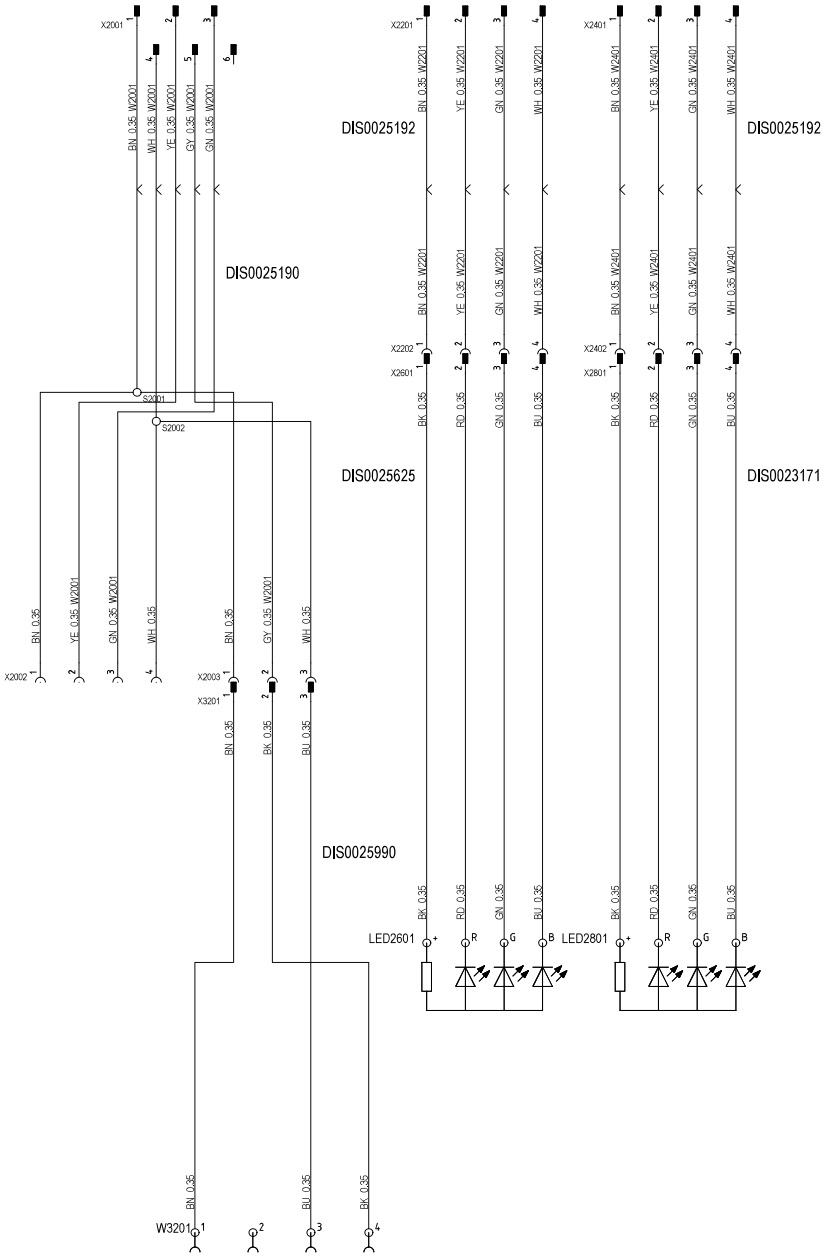



| REV. | MODIFICA | DATA | FIRME |
|---|---|---|---|
| 00 | Prima emissione | 22/08/25 | A. Goldoni |

Dis. N. SE000018
Rev. 00
Prog. N. PSL25-375

Impianto
OPTIMUS-XP

Descrizione
Schema elettrico Optimus-XP

Creato
19/06/25


Rilasciato
22/08/25

Esecutore
A. Goldoni

STEM S.r.l. Strada Ghiale, 12/B - 43014 - Medesano (PR) ITALY
Tel. 0525 - 43 01 02 - Fax 0525 - 42 13 41 www.stem.it

FOGLIO 2
SEGUE 3

QUESTO DISEGNO E' DI PROPRIETA' DELLA STEM S.r.l. CHE SE NE RISERVA I DIRITTI SANCITI DALLA LEGGE

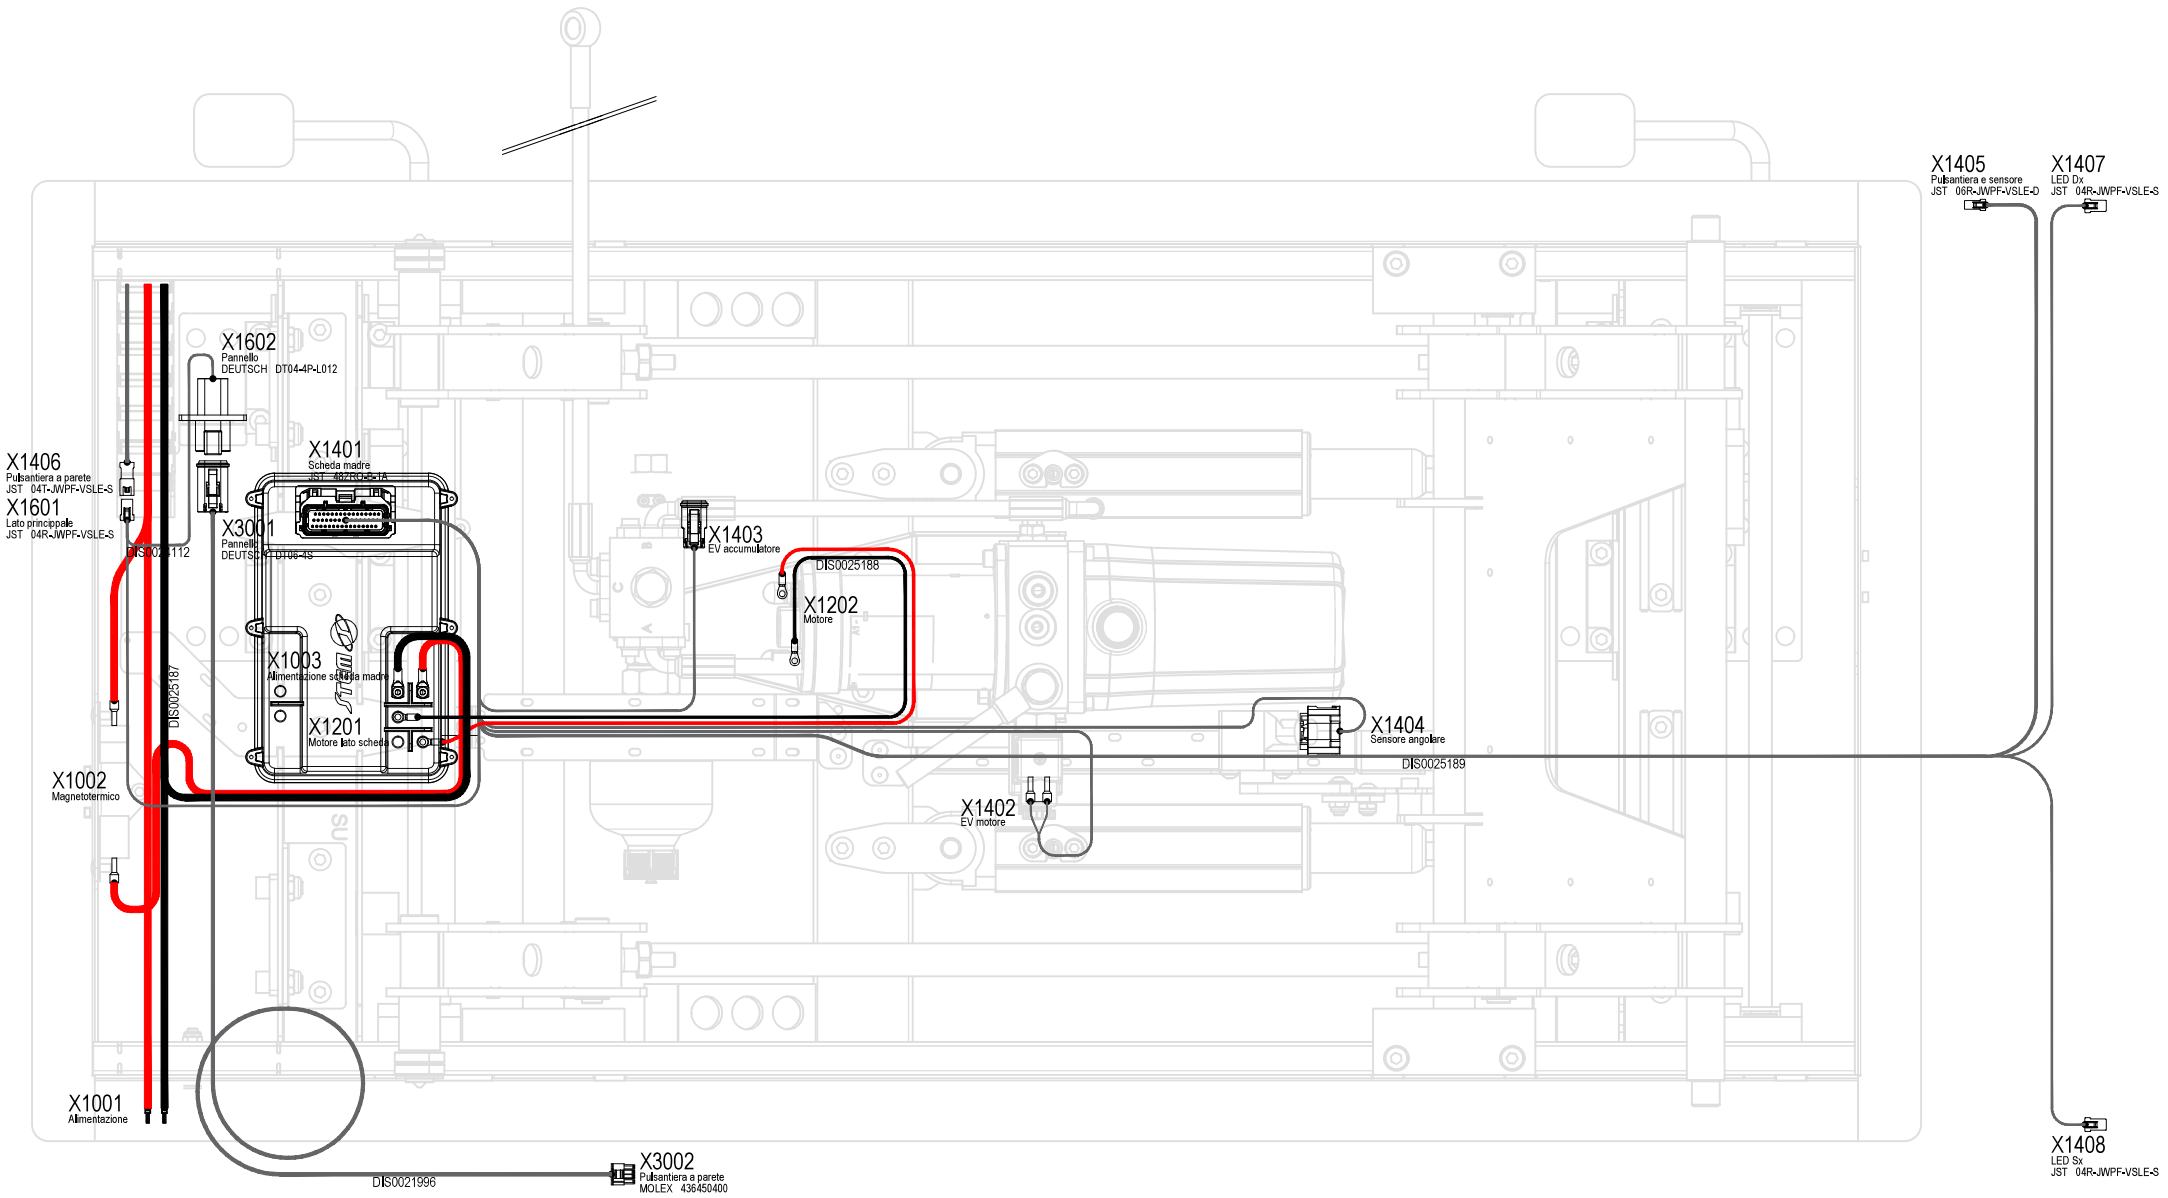


| REV. | MODIFICA | DATA | FIRME |
|---|---|---|---|
| 00 | Prima emissione | 22/08/25 | A. Goldoni |

Dis. N. SE000018
Rev. 00
Prog. N. PSL25-375

Impianto
OPTIMUS-XP

Descrizione
Schema elettrico Optimus-XP

Creato
19/06/25

Rilasciato
22/08/25


Esecutore
A. Goldoni

STEM S.r.l. Strada Ghisle, 12/B - 43014 - Medesano (PR) ITALY
Tel. 0525 - 43 01 02 - Fax 0525 - 42 13 41 www.stem.it

FOGLIO 3

SEGUE 4

QUESTO DISEGNO E' DI PROPRIETA' DELLA STEM S.r.l. CHE SE NE RISERVA I DIRITTI SANCITI DALLA LEGGE

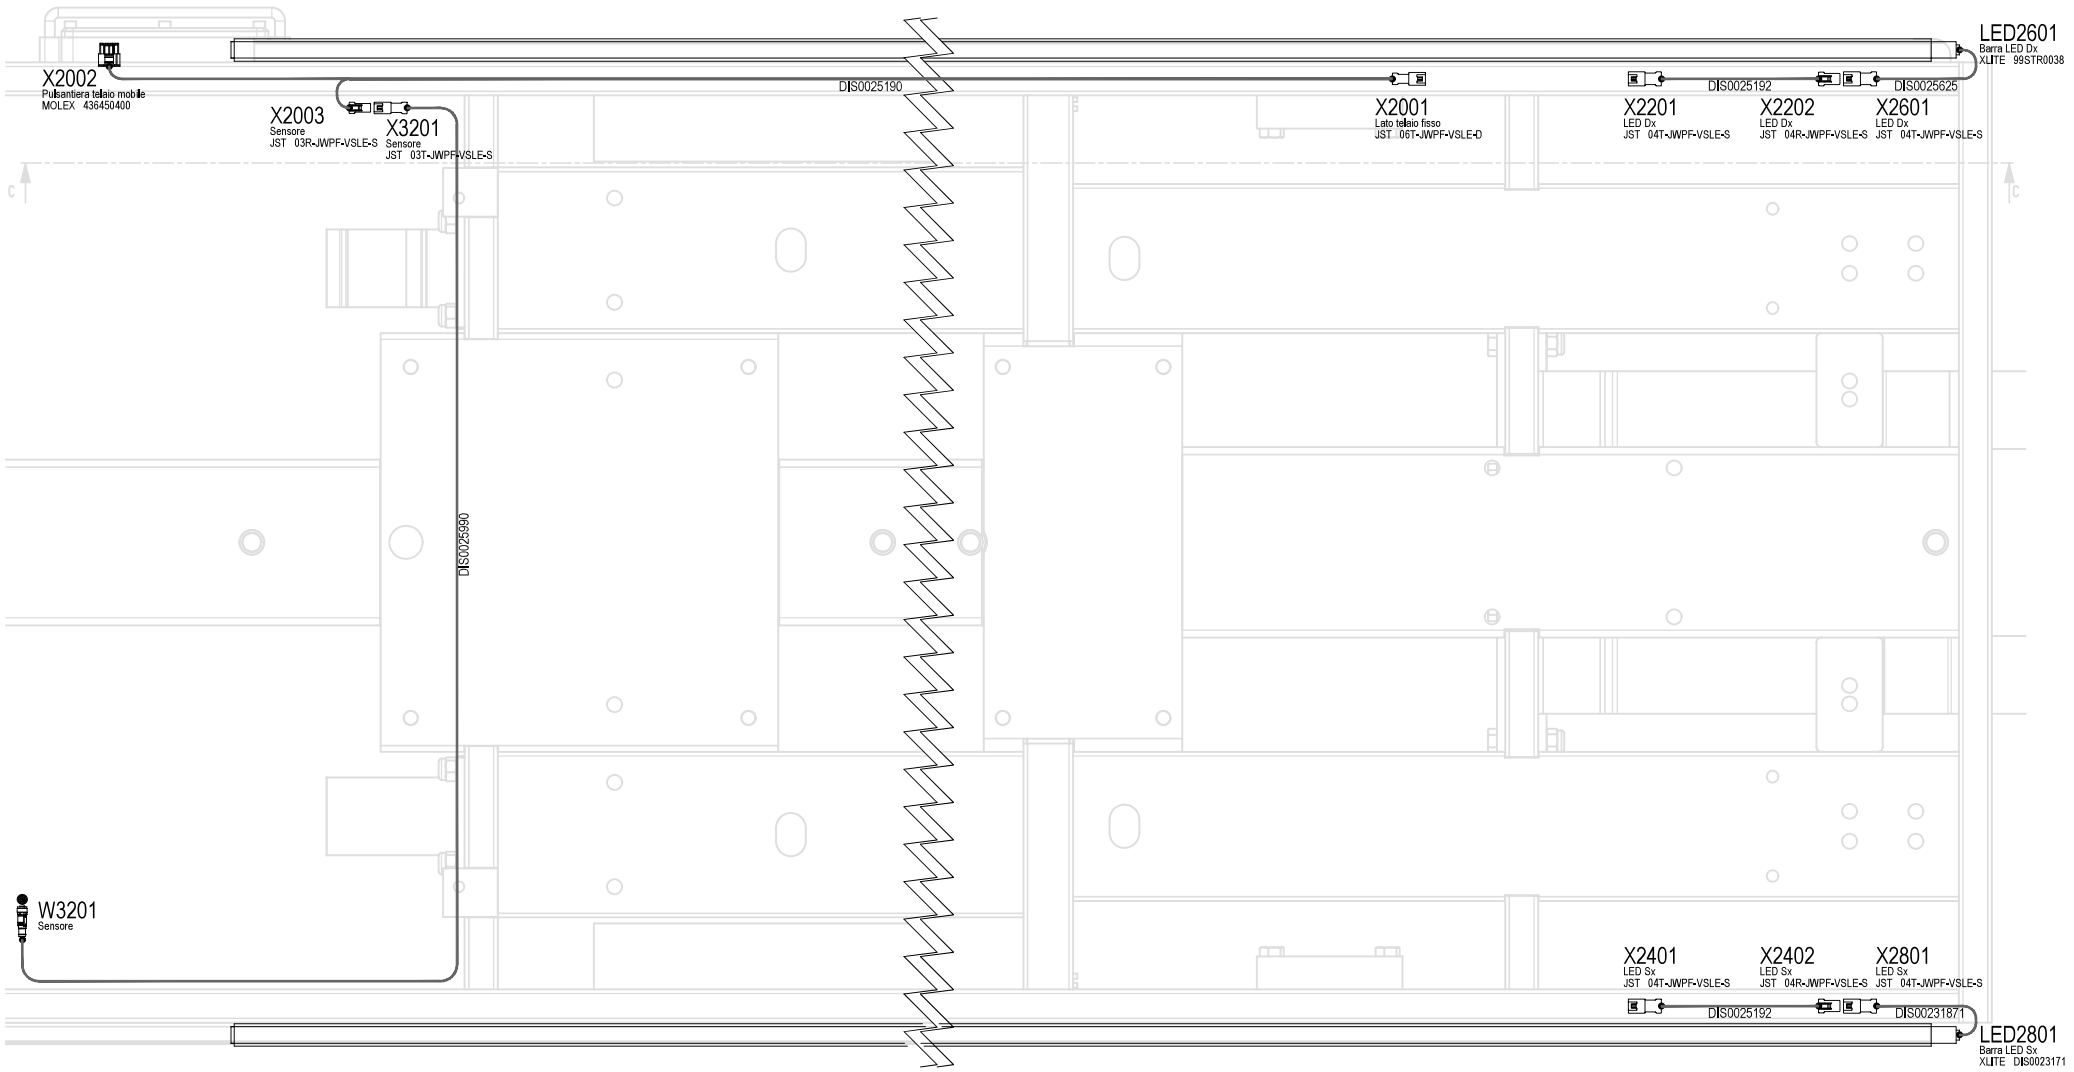


| REV. | MODIFICA | DATA | FIRME |
|---|---|---|---|
| 00 | Prima emissione | 22/08/25 | A. Goldoni |

Dis. N. SE000018
Rev. 00
Prog. N. PSL25-375

Impianto
OPTIMUS-XP

Descrizione
Schema elettrico Optimus-XP

Creato
19/06/25

Rilasciato
22/08/25

Esecutore
A. Goldoni

STEM S.r.l. Strada Ghiaie, 12/B - 43014 - Medesano (PR) ITALY
Tel. 0525 - 43 01 02 - Fax 0525 - 42 13 41 www.stem.it

FOGLIO 4

SEGUE /

QUESTO DISEGNO E' DI PROPRIETA' DELLA STEM S.r.l. CHE SE NE RISERVA I DIRITTI SANCITI DALLA LEGGE